

外構ロボット設計案

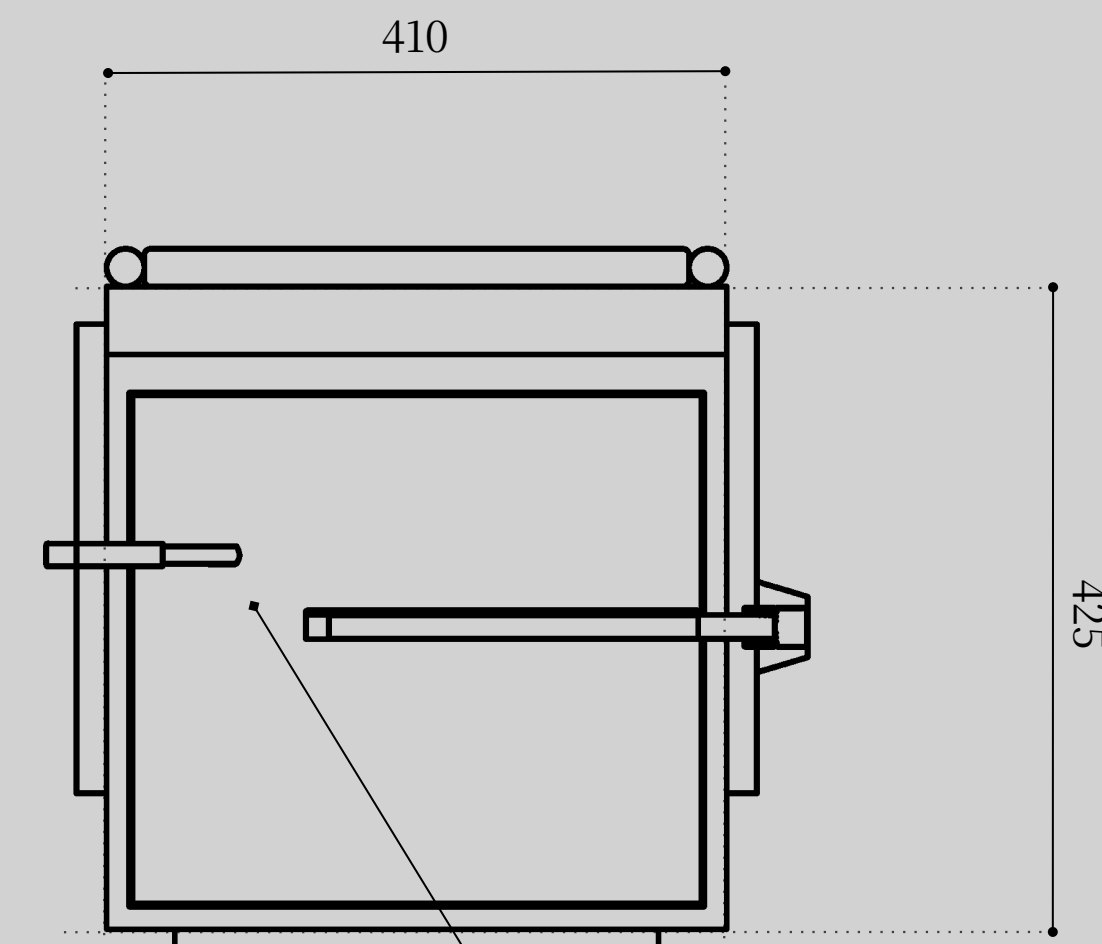


図4-1 1/5 平面図

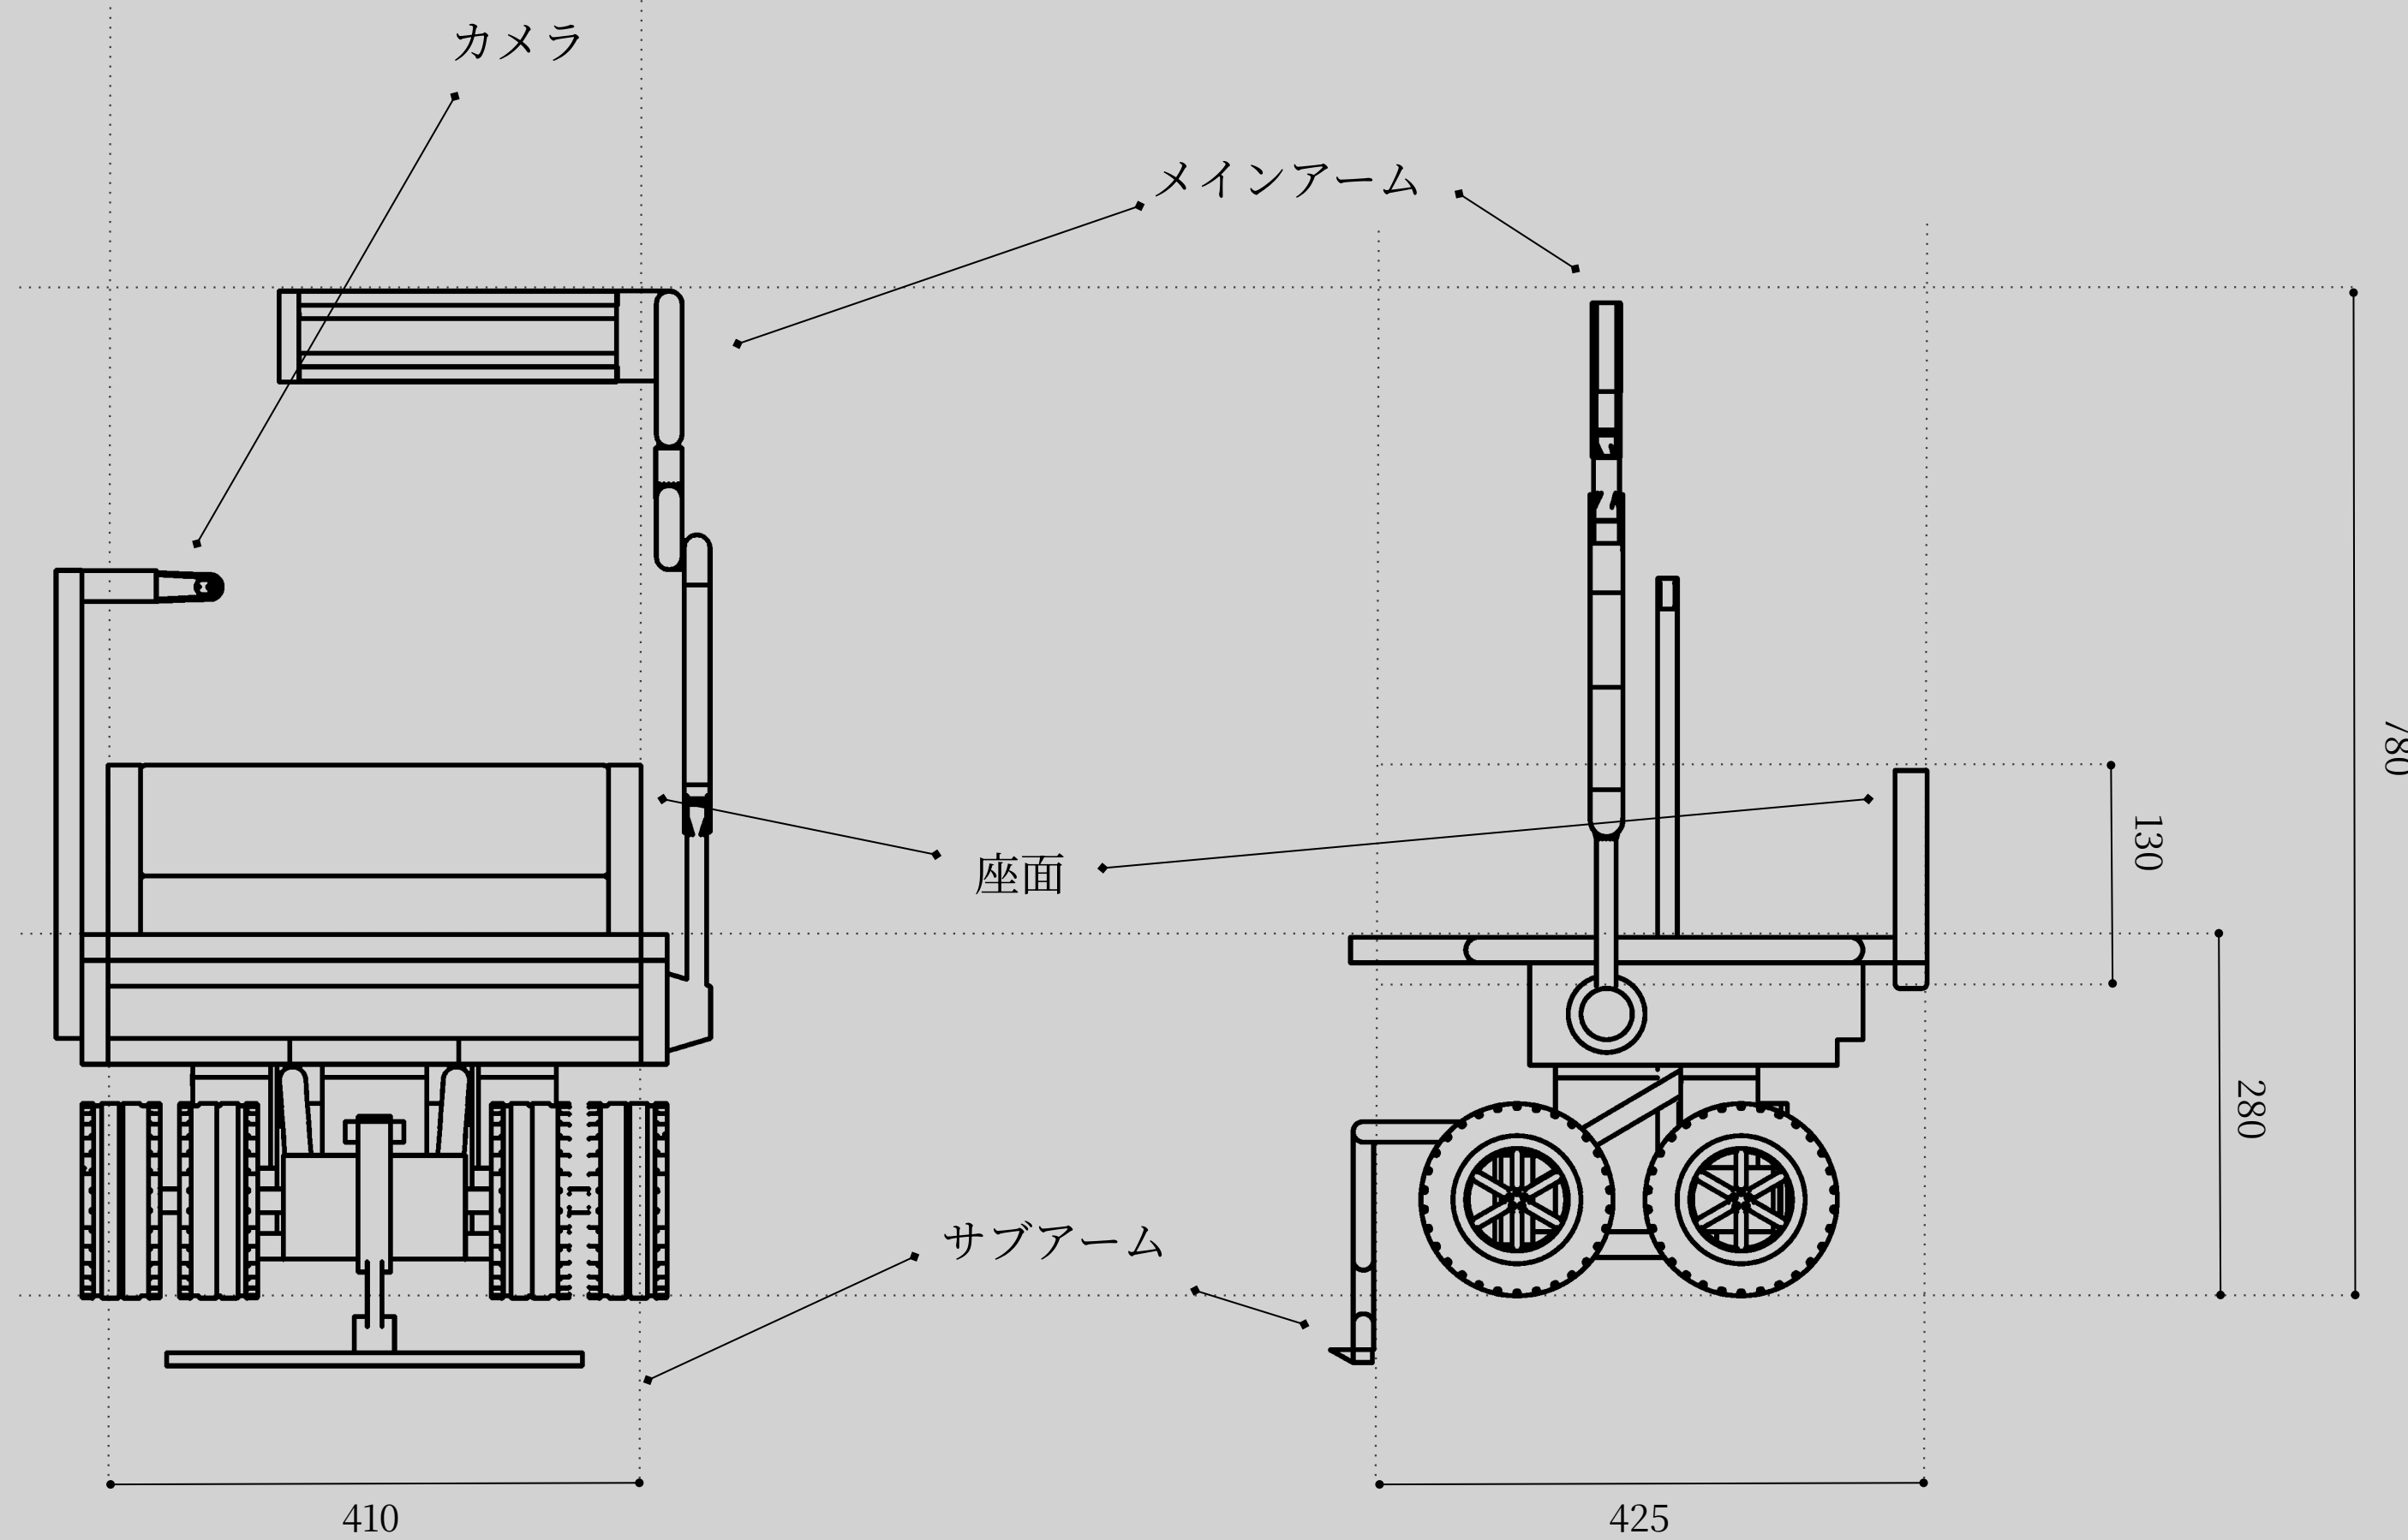


図4-2 1/5 前面立面図

外構ロボットは，その場面によって自律的に変化するエクステリアである．椅子・ラック・塀などとしてふるまい，狭隘道路と敷地を緩やかにつなぐ存在となる．

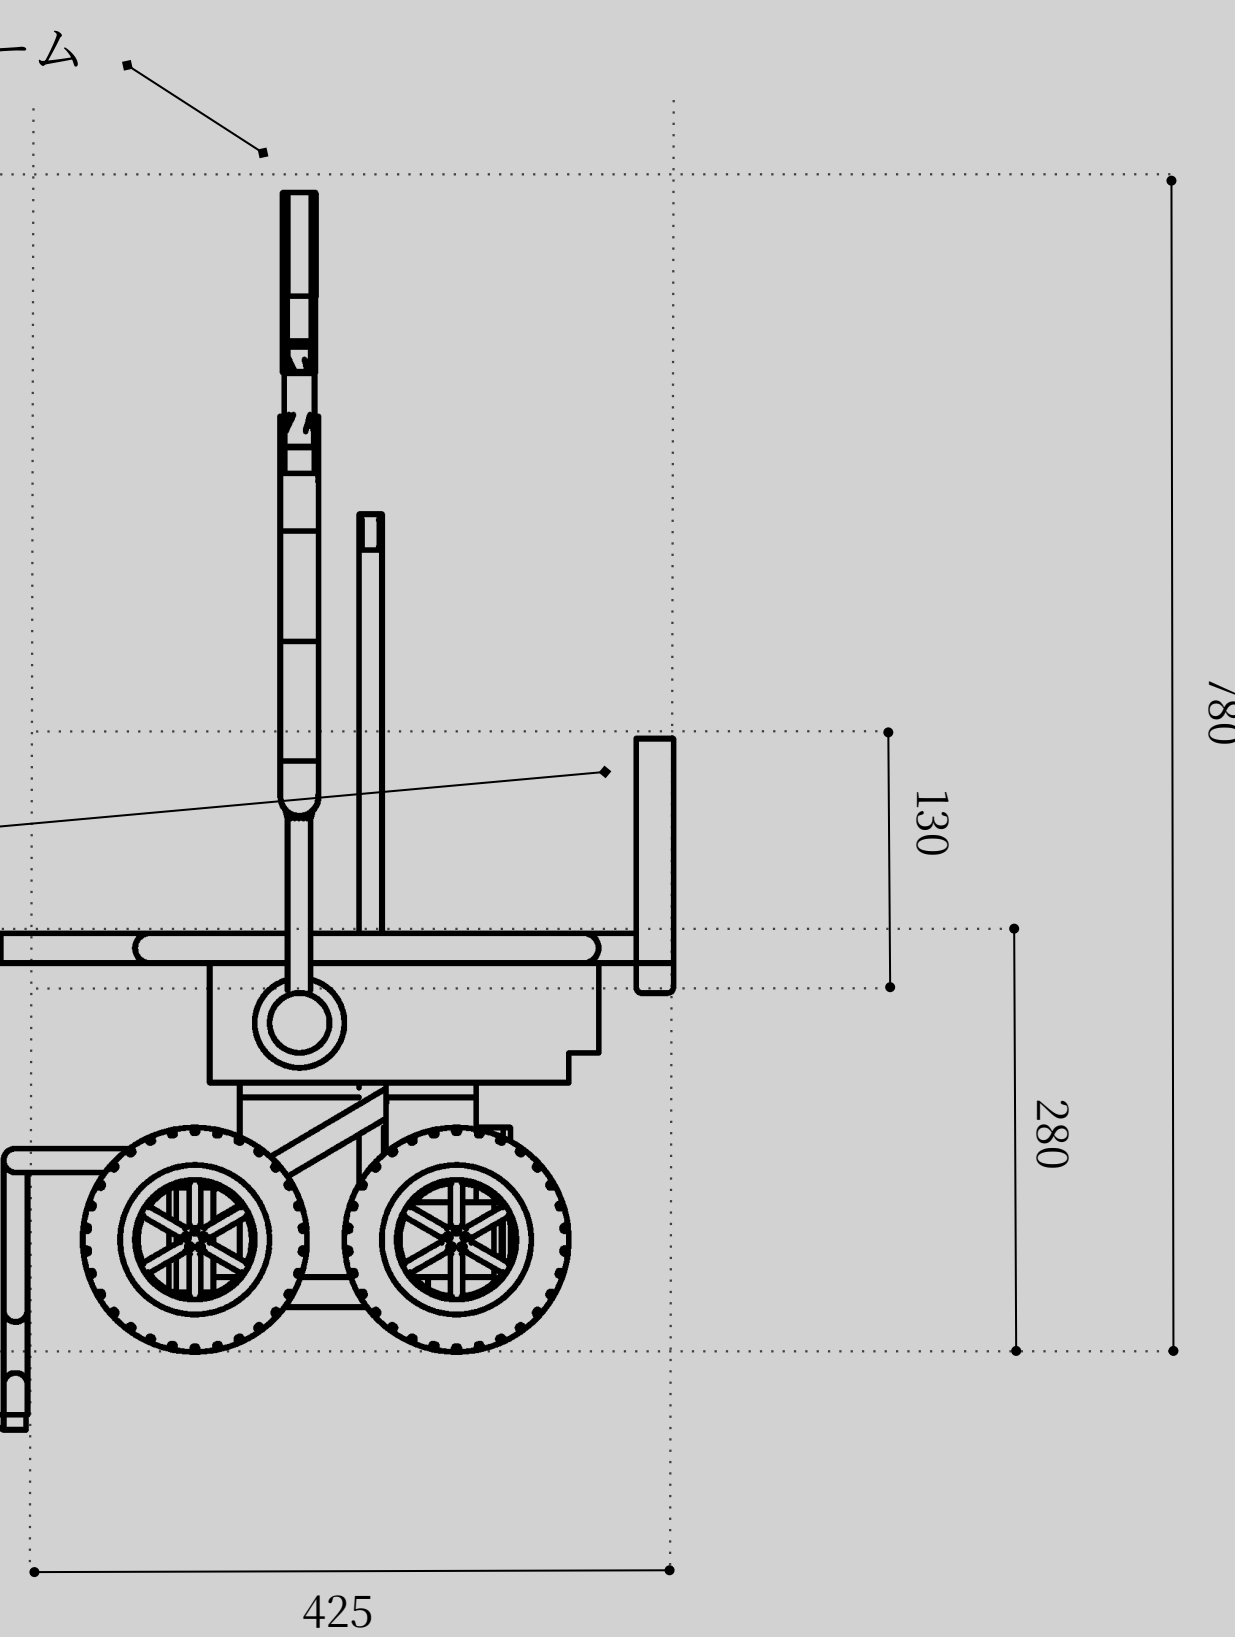


図4-3 1/5 右面立面図

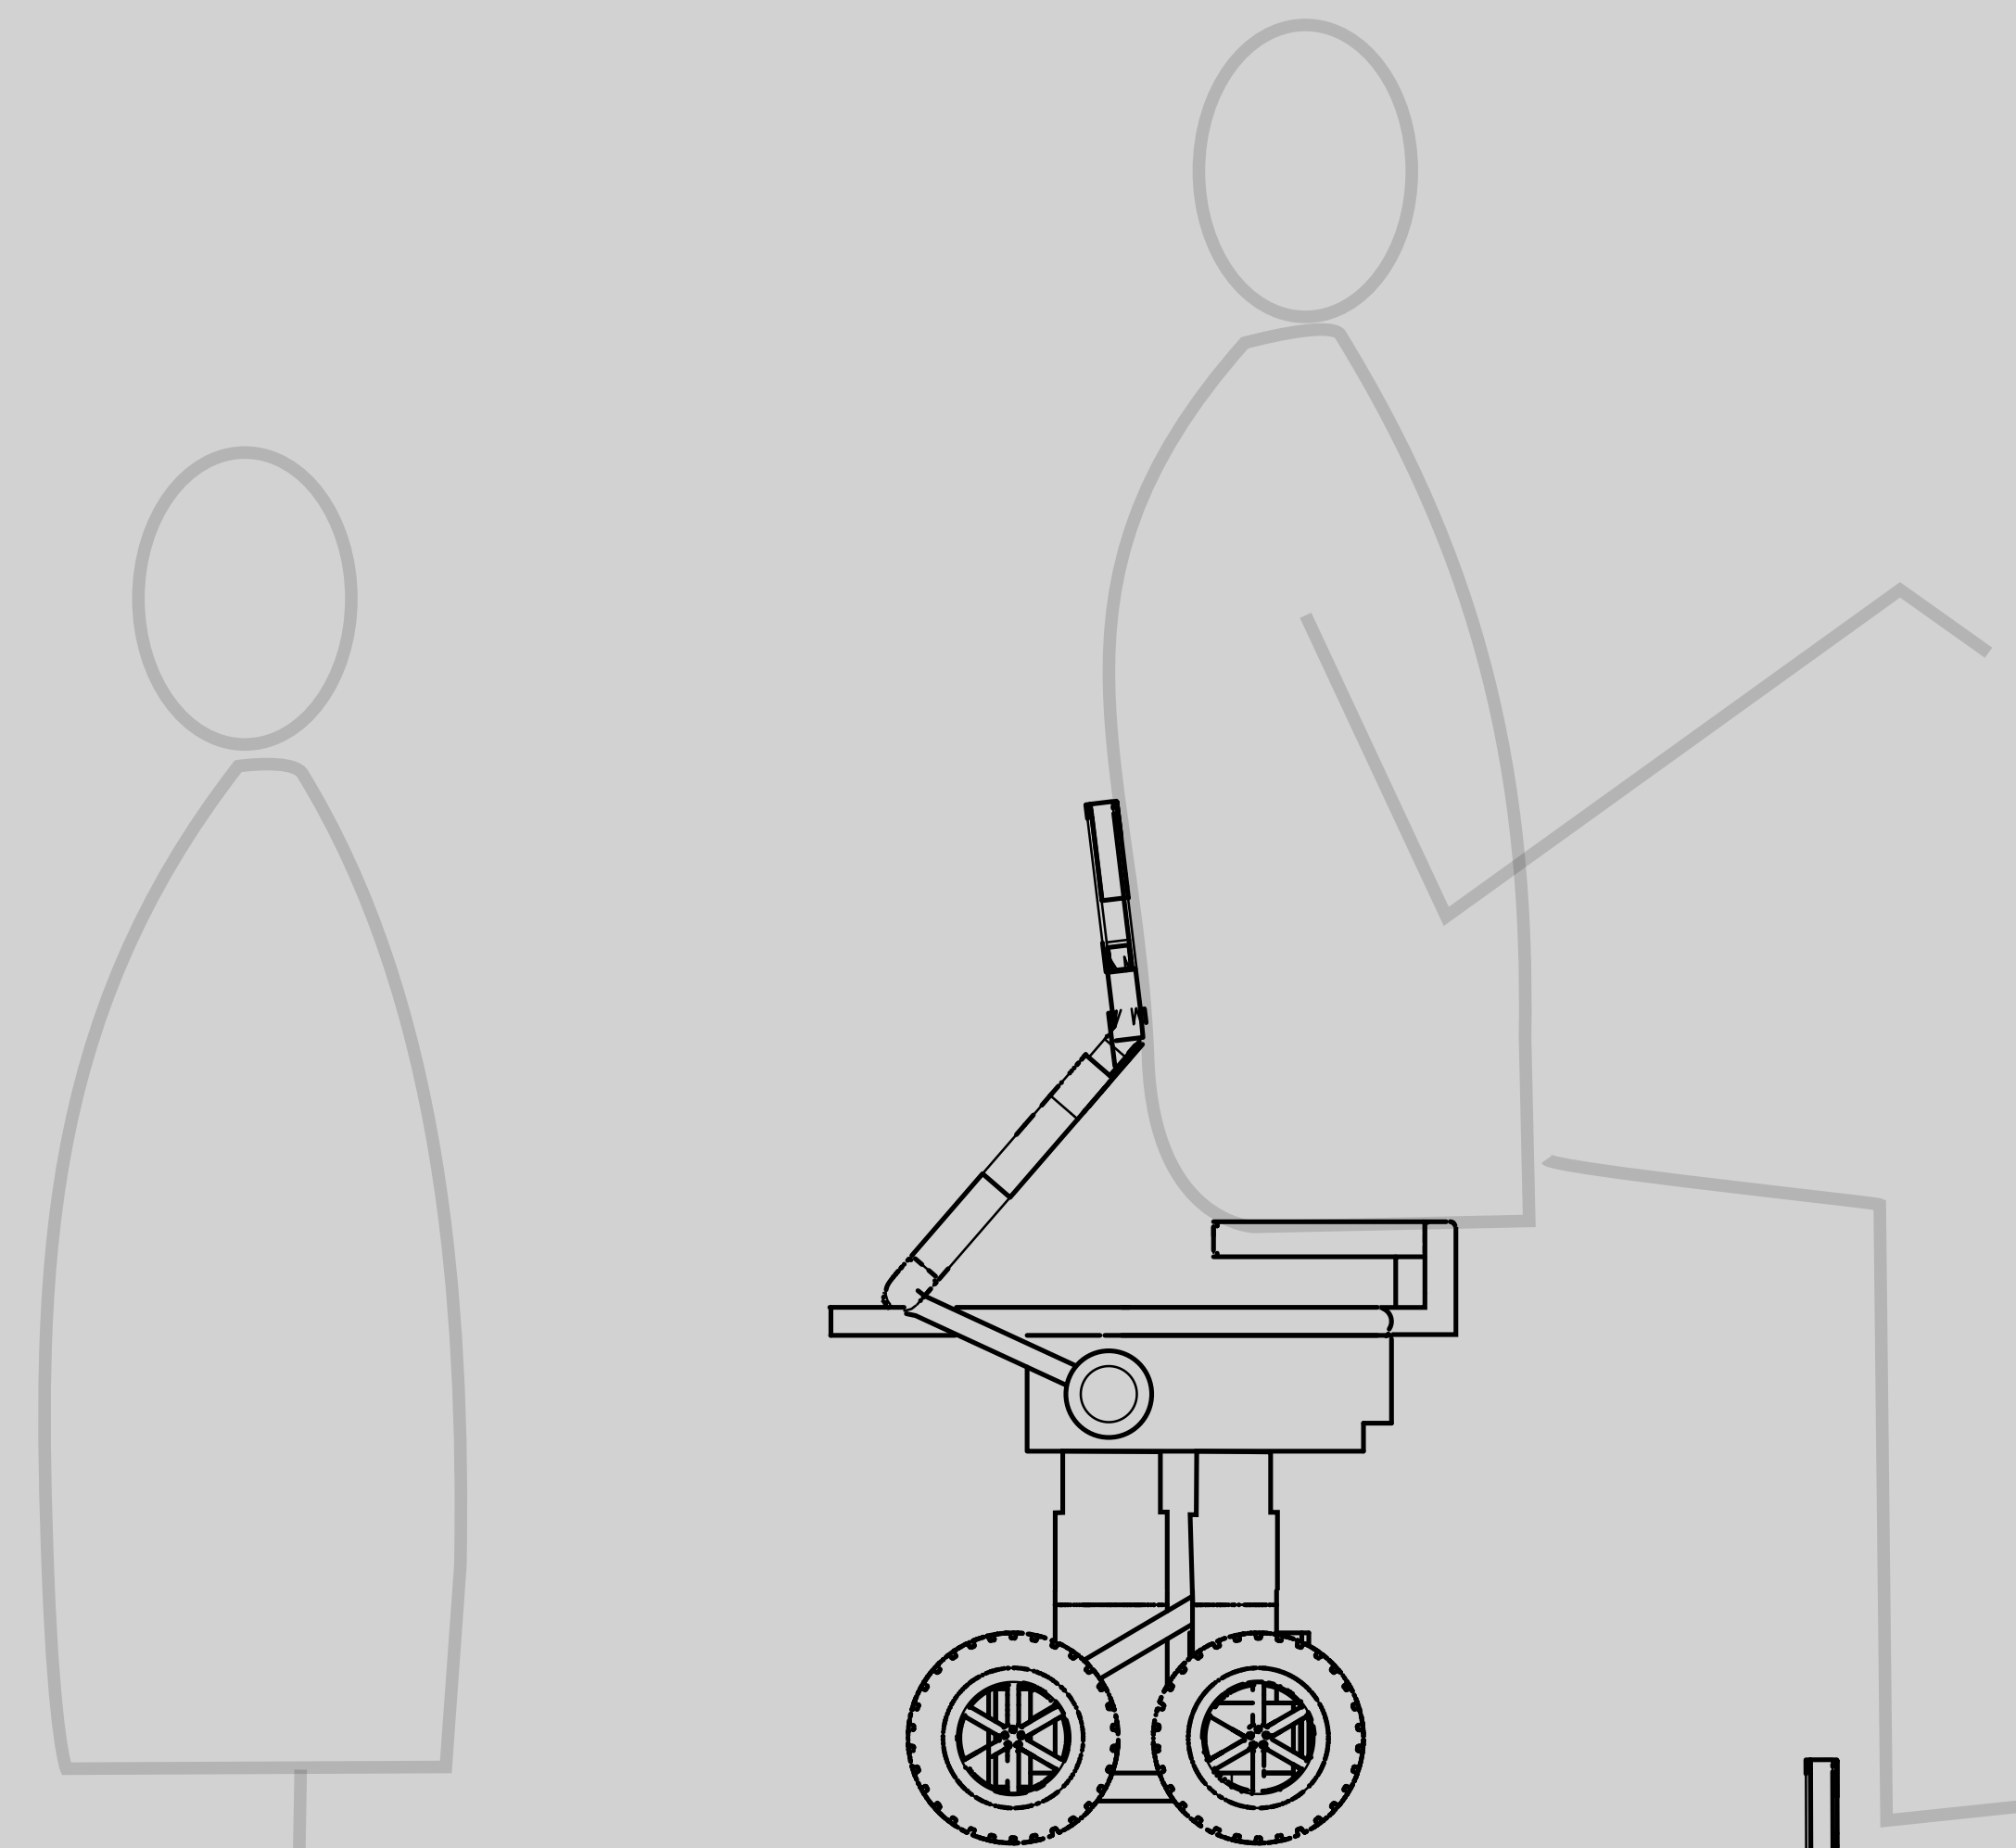


図4-4 椅子として

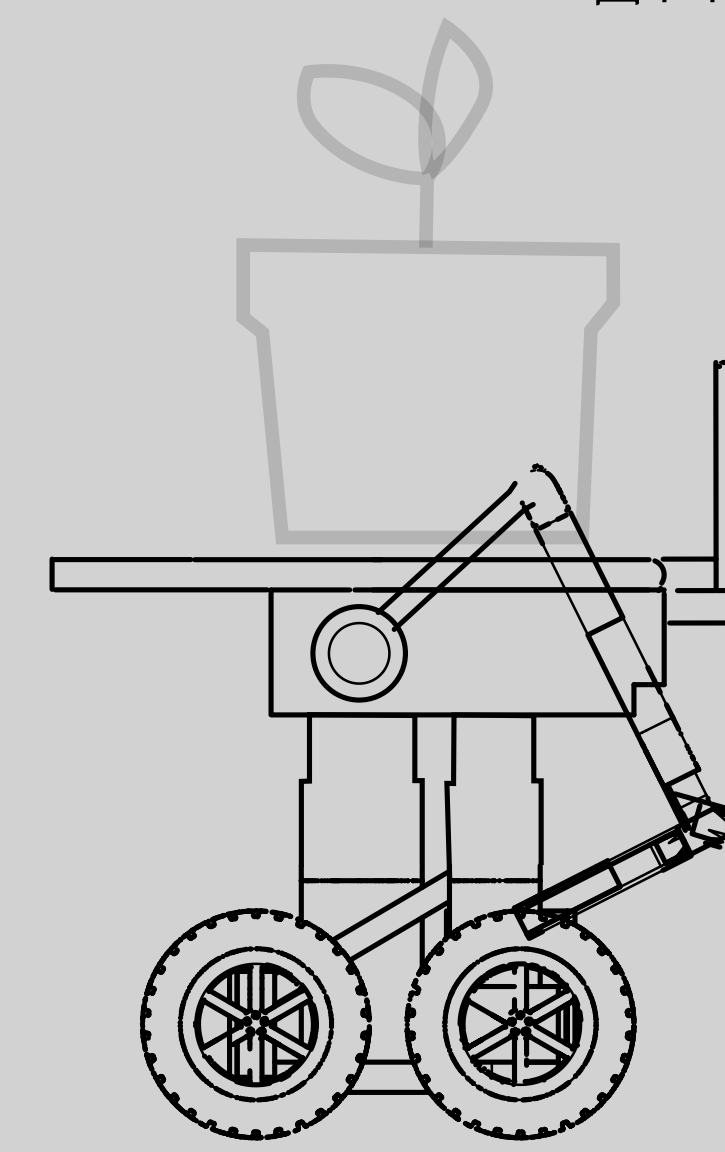


図4-5 屋外用ラックとして

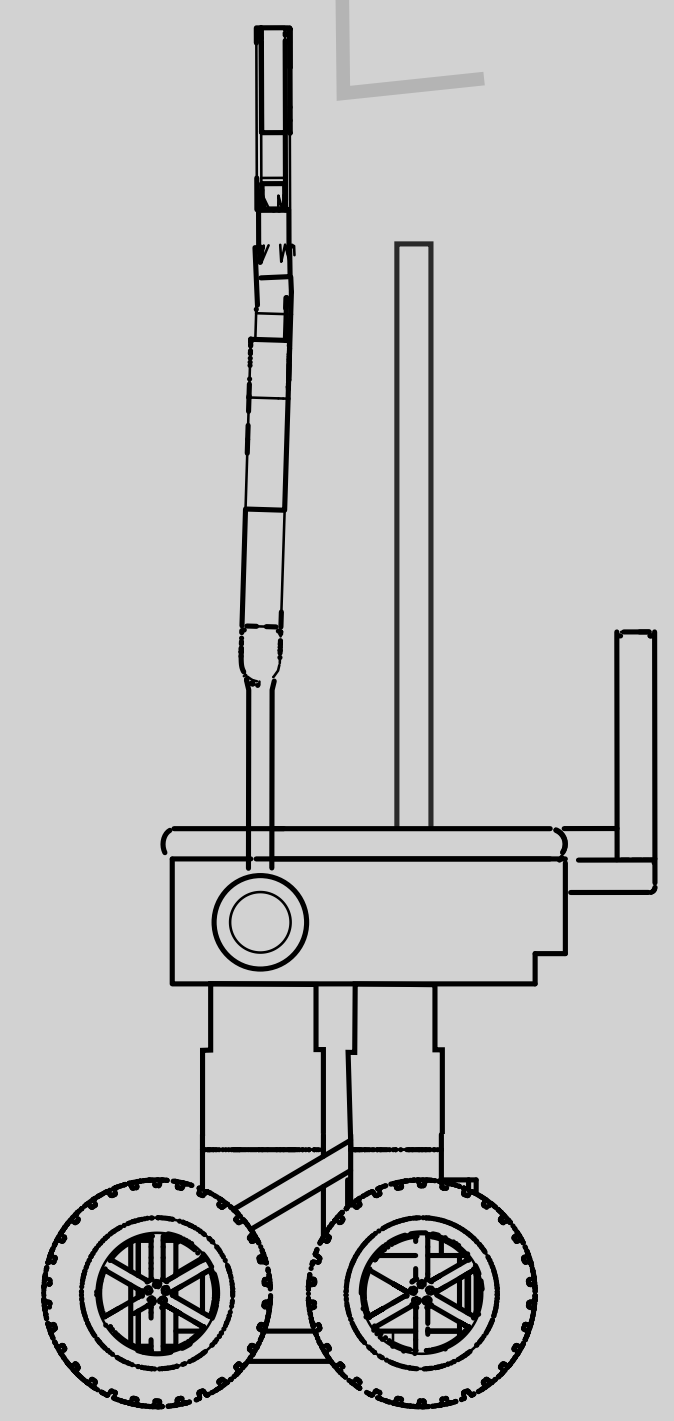


図4-6 塀として